


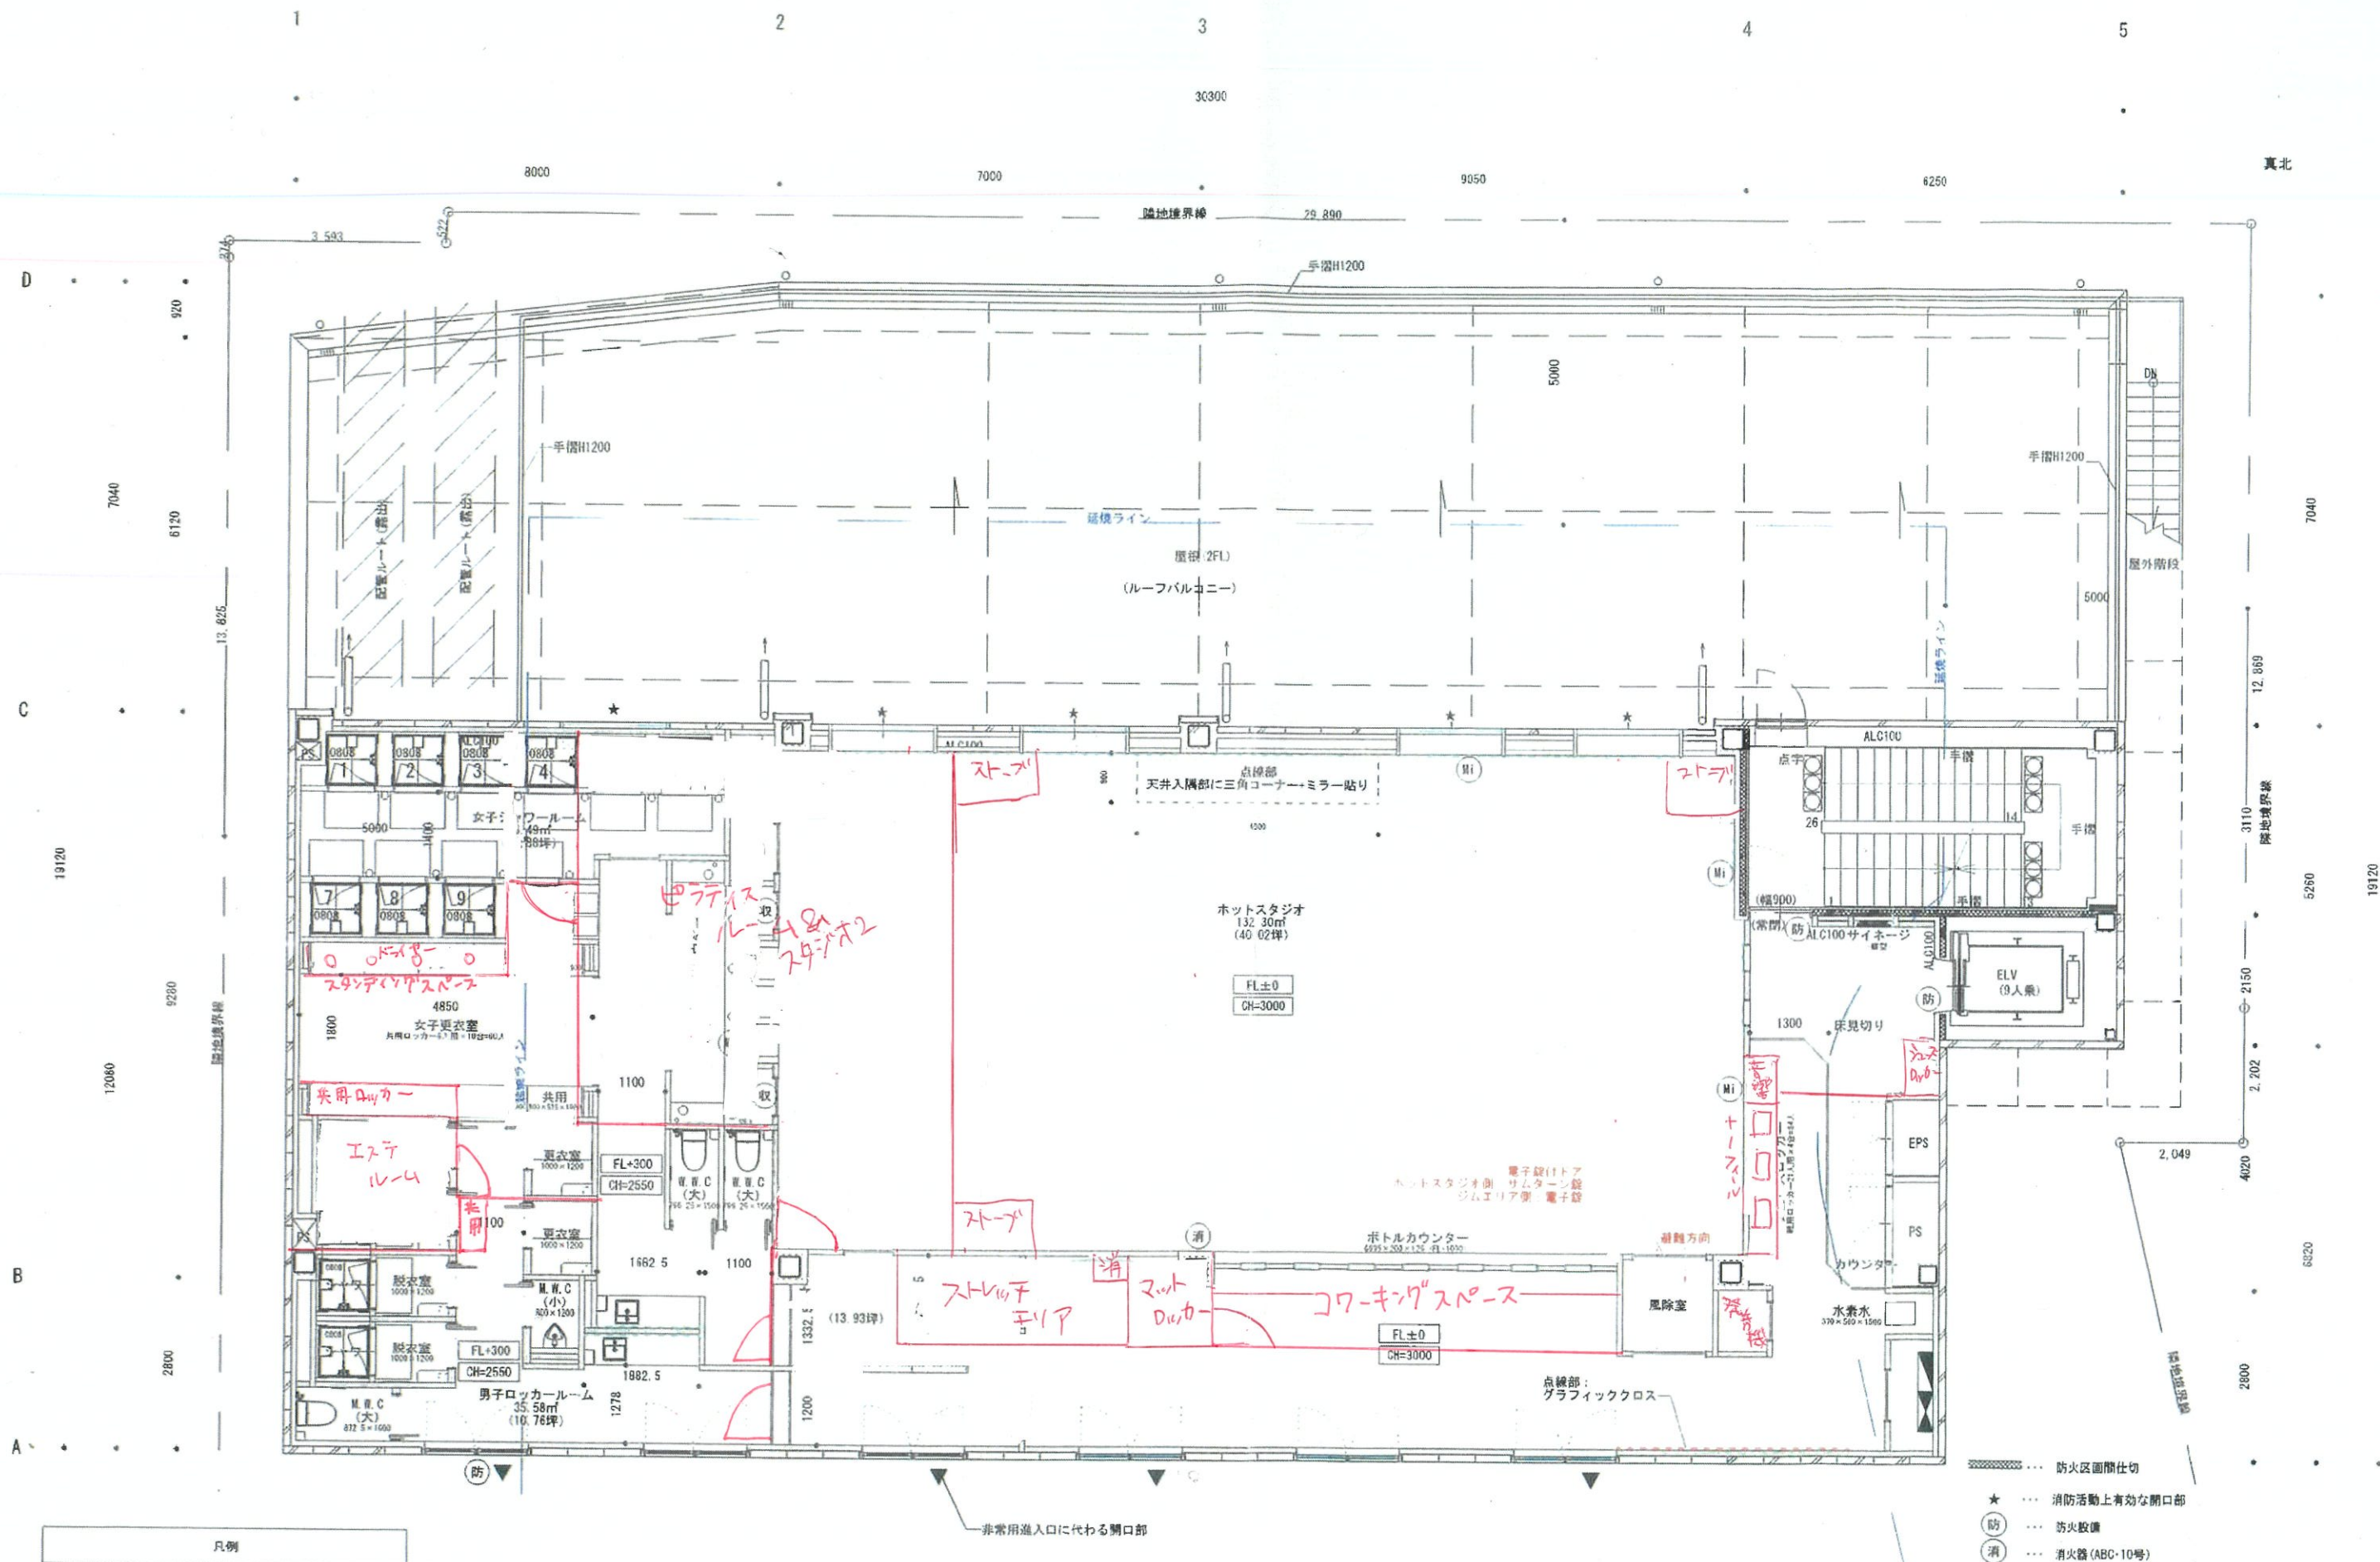

凡例	
(M)	ミラー貼り
(G)	ガラス・ガラス戸
(掃)	掃除用具入れ
(収)	収納

店舗面積 (共用階段、ELV除く現況内寸法)	93.55坪 (309.27㎡)
積載荷重 300kg/㎡	
※合計面積は賃貸契約面積と違ってきます。	

2017.05.25 2017.05.18 2017.05.12 Revised Date	株式会社 C&P マネジメント 2F AKASAKA-BT BLDG. 1-4-SAKASAKA, MINATO-KU, TOKYO 〒107-0052 TEL: 03-5575-5213/FAX: 03-5575-5214 URL: http://www.cm-pm.jp	PROJECT (仮称) JOYFIT24 経営 新装工事 CHECK:	TITLE: 3F: 平面図 SCALE: S=1/100 DATE: 2017.03.15	No: A-07
--	--	---	--	----------