


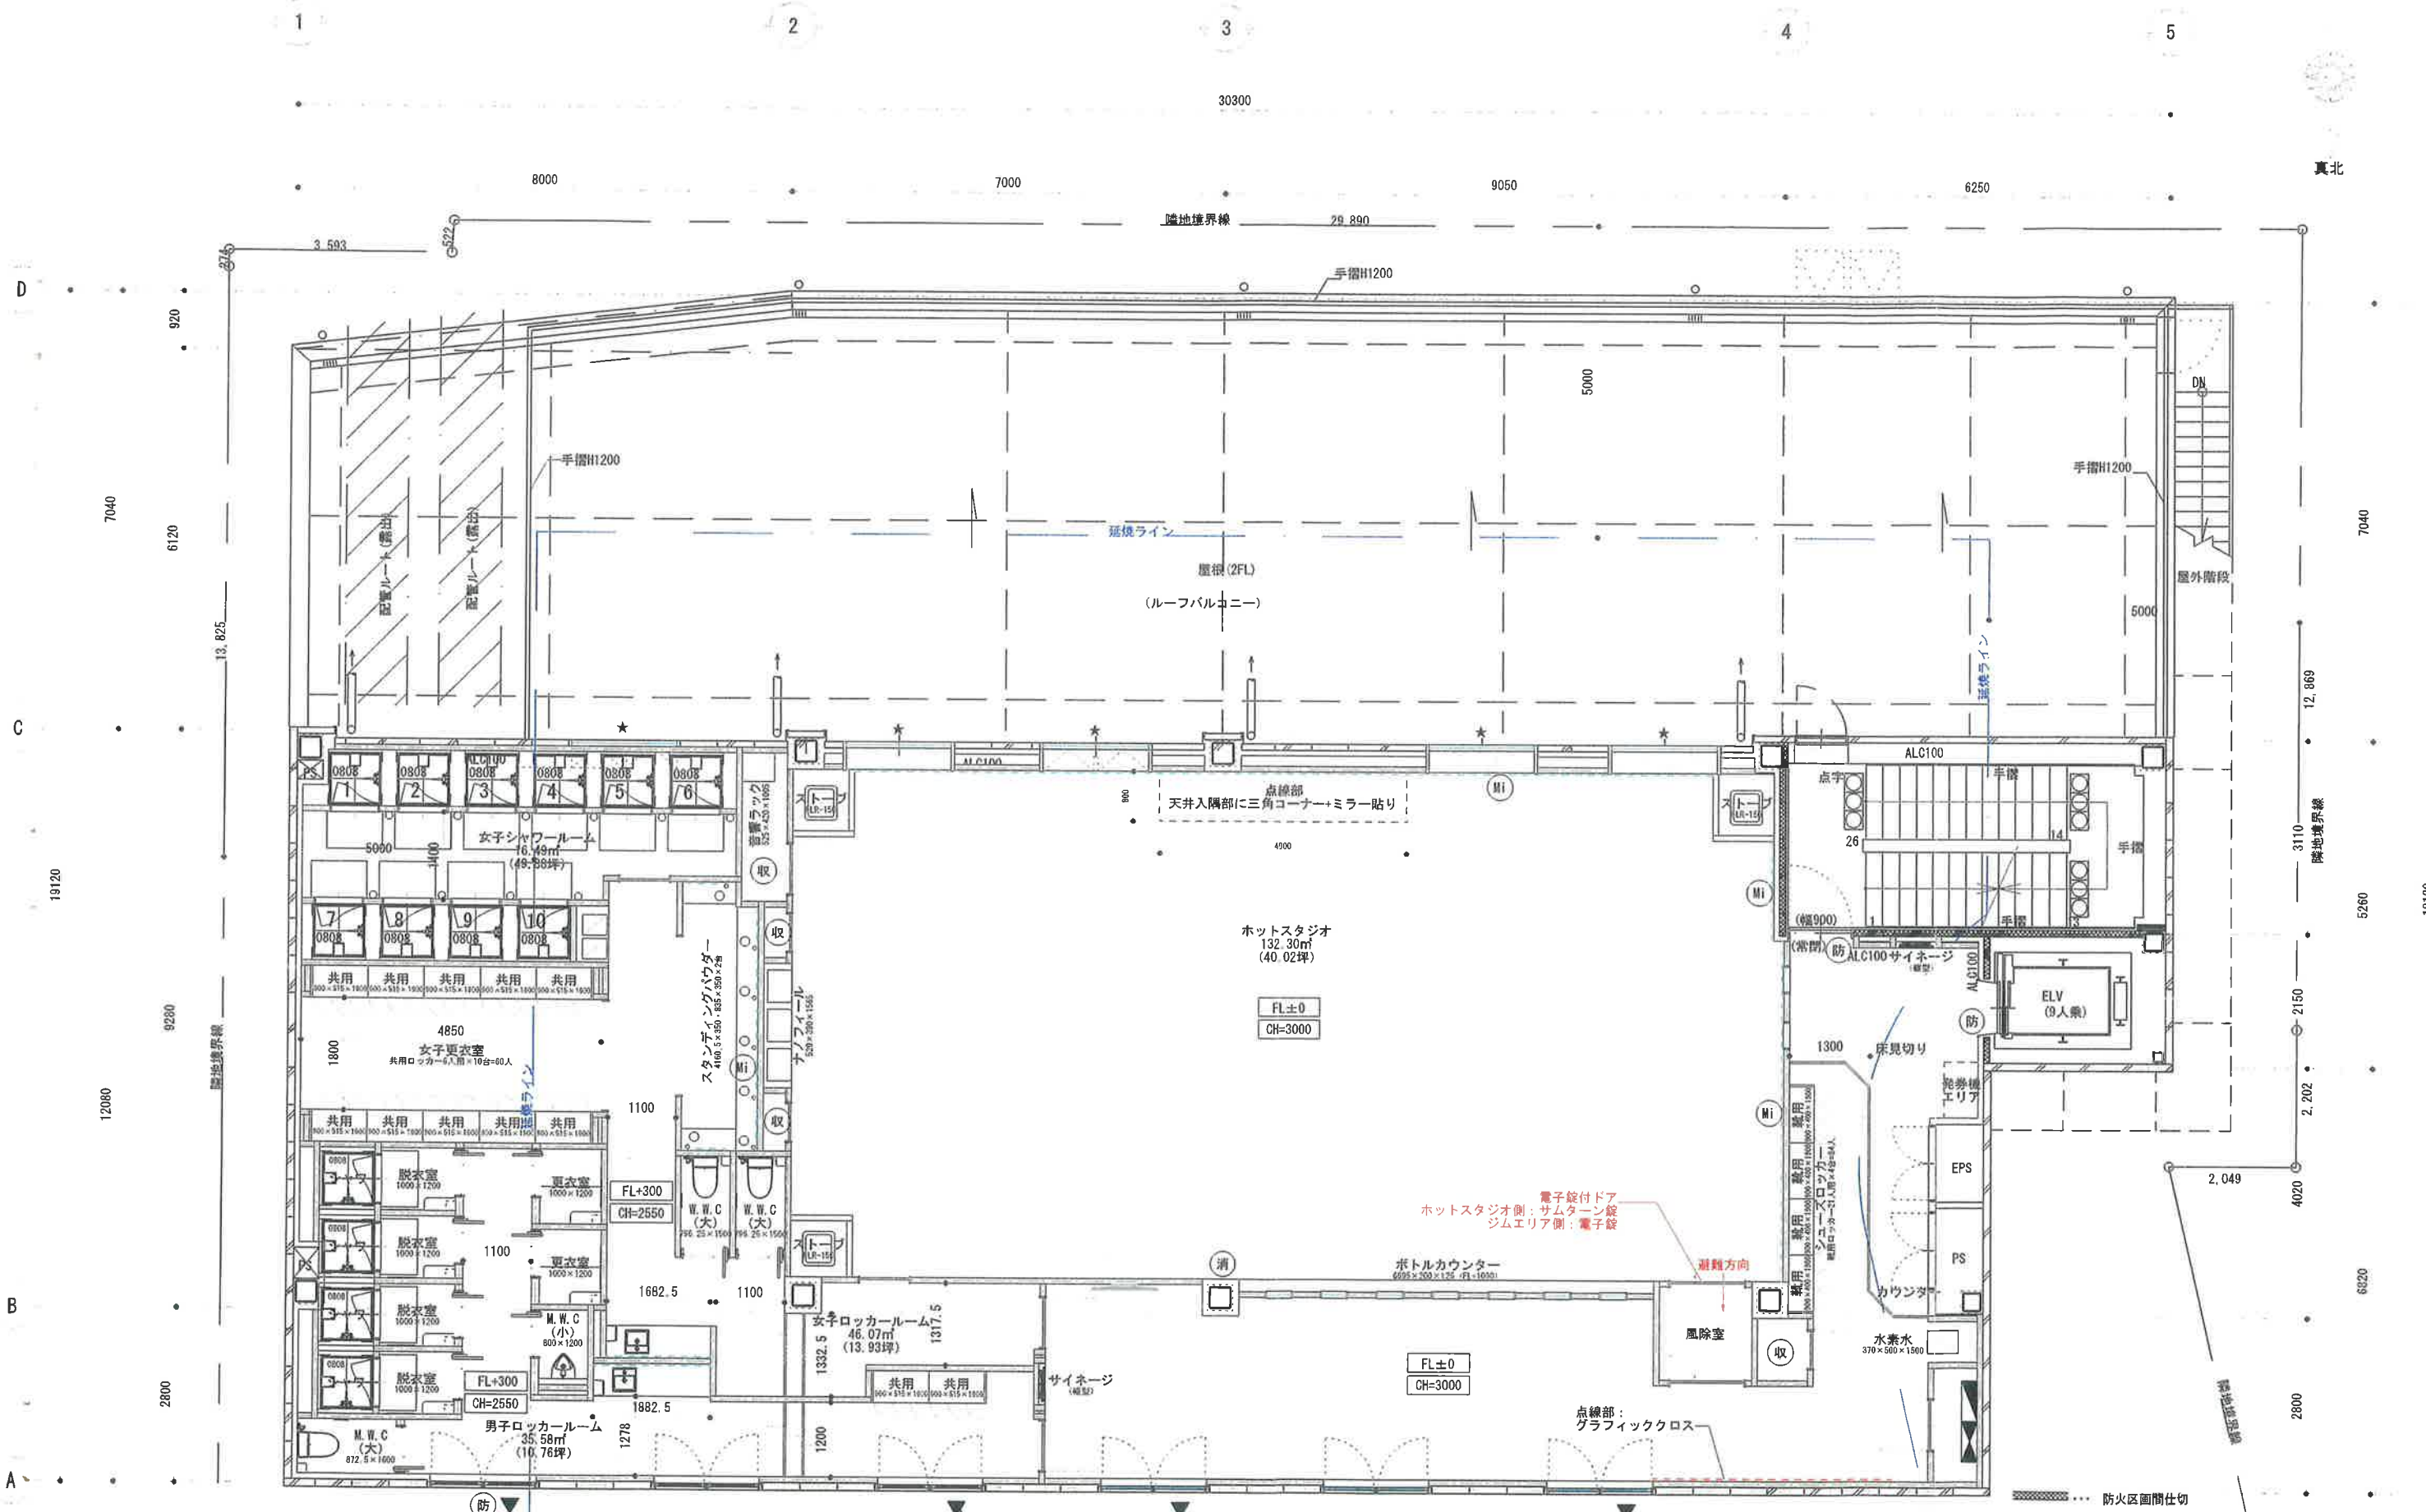

凡例	
(Mi)	ミラー貼り
(G)	ガラス有・ガラス戸
(掃)	掃除用具入れ
(取)	収納

店舗面積 (共用階段、ELV除く現況内寸法)	93.55坪 (309.27m²)
積載荷重 300kg/m²	

※合計面積は賃貸契約面積と違っています。

2017.05.25 2017.05.18 2017.05.12 Revised Date	C&P MANAGEMENT 株式会社 C&Pマネジメント 2F AKASAKA-BT BLDG, 1-4-8AKASAKA, MINATO-KU, TOKYO 〒107-0052 TEL:03-5575-5213/FAX:03-5575-5214 URL: http://www.cm-pm.jp	PROJECT: (仮称) JOYFIT24経営 新装工事 CHECK:	TITLE: 3F: 平面図 SCALE: S=1/100 DATE: 2017.03.15	No: A-07
--	---	---	--	----------

- ... 防火区画間仕切り
- ★ ... 消防活動上有効な開口部
- (防) ... 防火設備
- (消) ... 消火器(ABC・10号)