


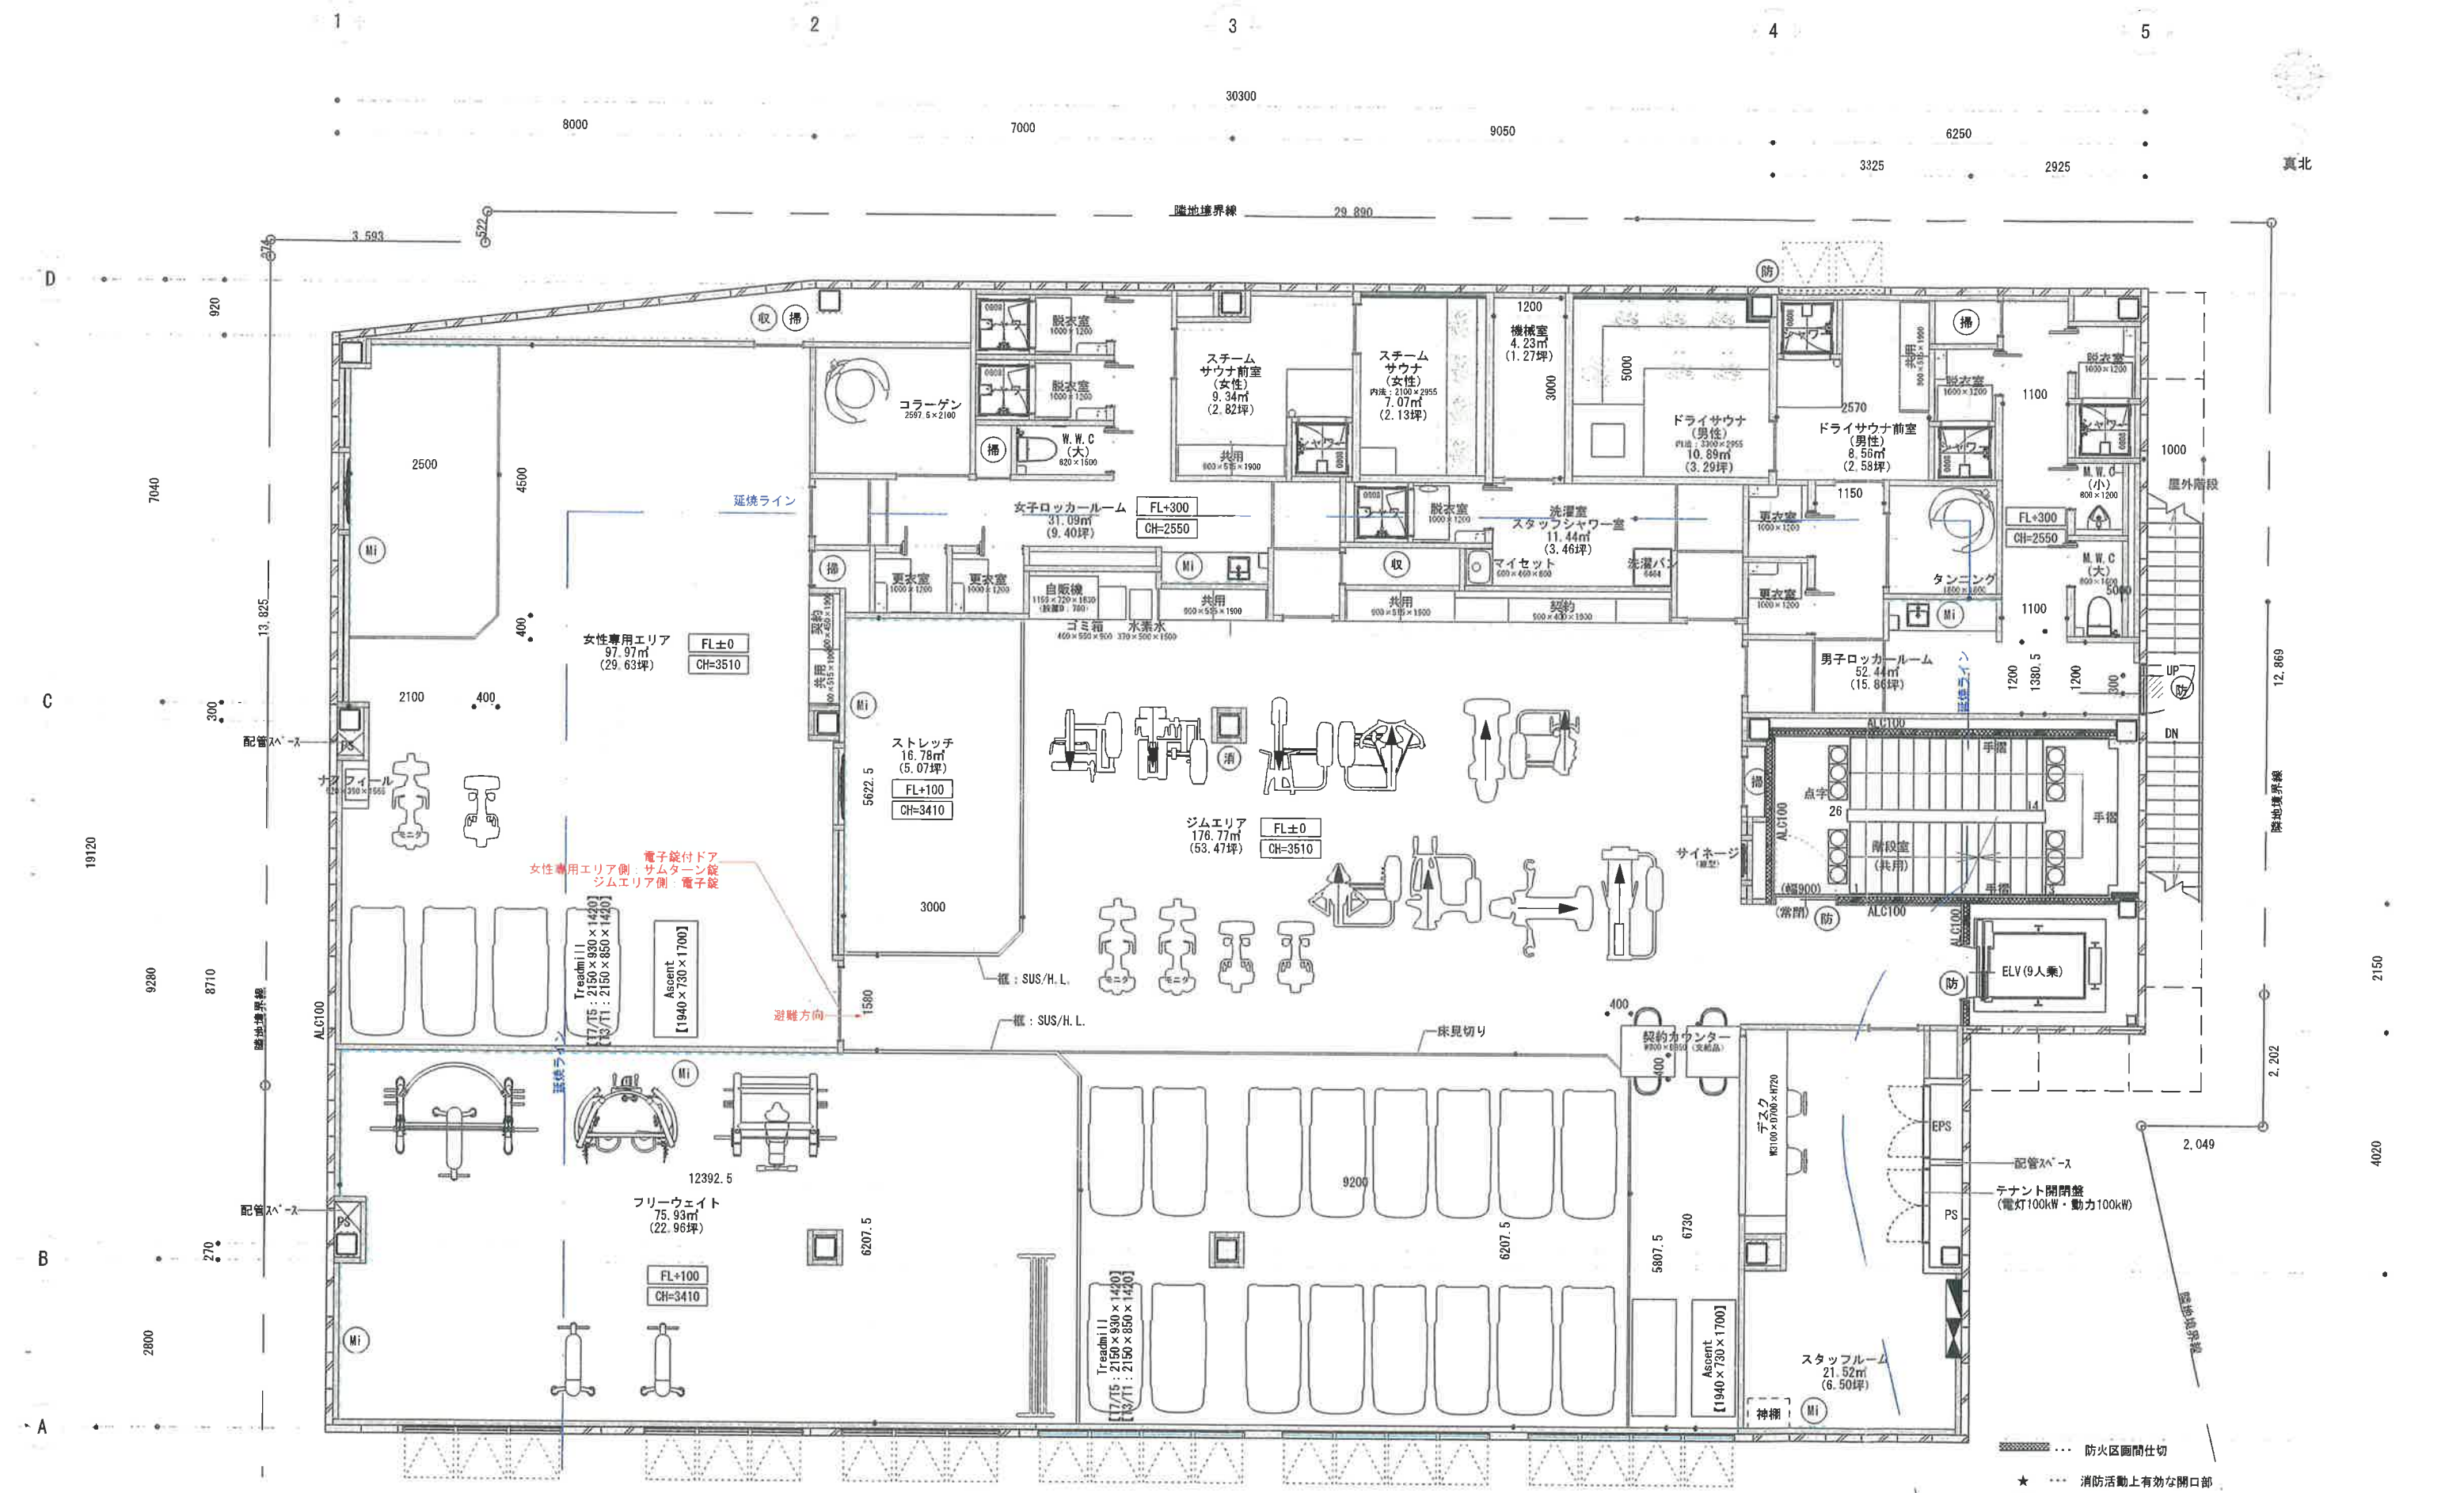

凡例	
(Mi)	ミラー貼り
(G)	ガラス有・ガラス戸
(掃)	掃除用具入れ
(収)	収納

店舗面積 (共用階段、ELV除く現況内寸法)	158.87坪 (525.21㎡)
積載荷重 400kg/㎡	

※合計面積は賃貸契約面積と違っています。

- 防火区画間仕切
- 消防活動上有効な開口部
- 防火設備
- 消火器 (ABC-10号)

2017.05.23
Revised Date

C&P
MANAGEMENT

株式会社 C&Pマネジメント
2F AKASAKA-BT BLDG.
1-4-BAKASAKA, MINATO-KU, TOKYO
〒107-0052 TEL:03-5575-5213/FAX:03-5575-5214
URL: <http://www.cmpm.jp>

PROJECT (仮称) JOYFIT24経堂 新装工事
CHECK :
SCALE : S=1/100
DATE : 2017.03.15

TITLE 2F : 平面図
No : A-06