

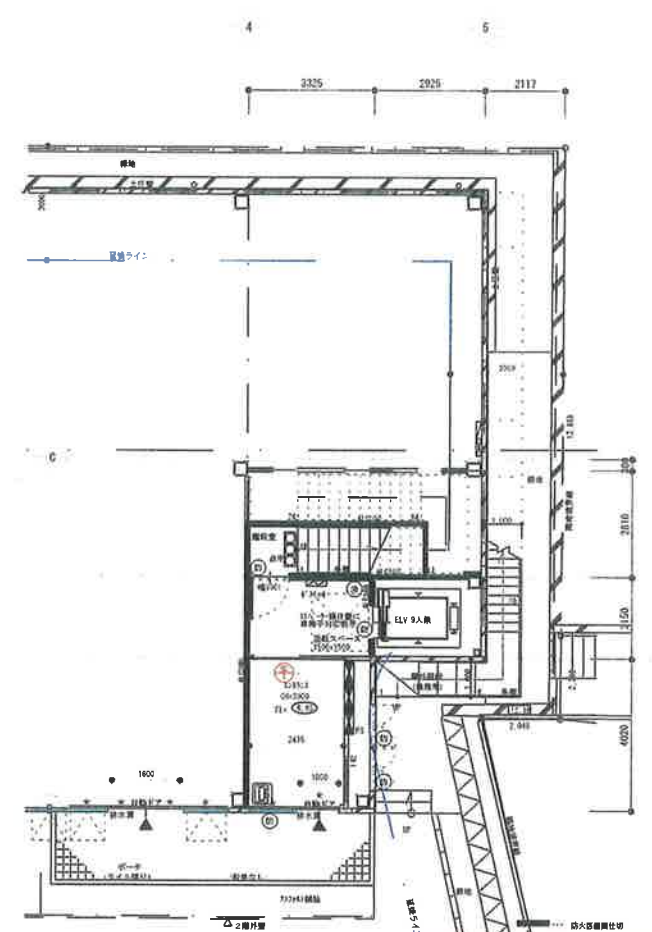


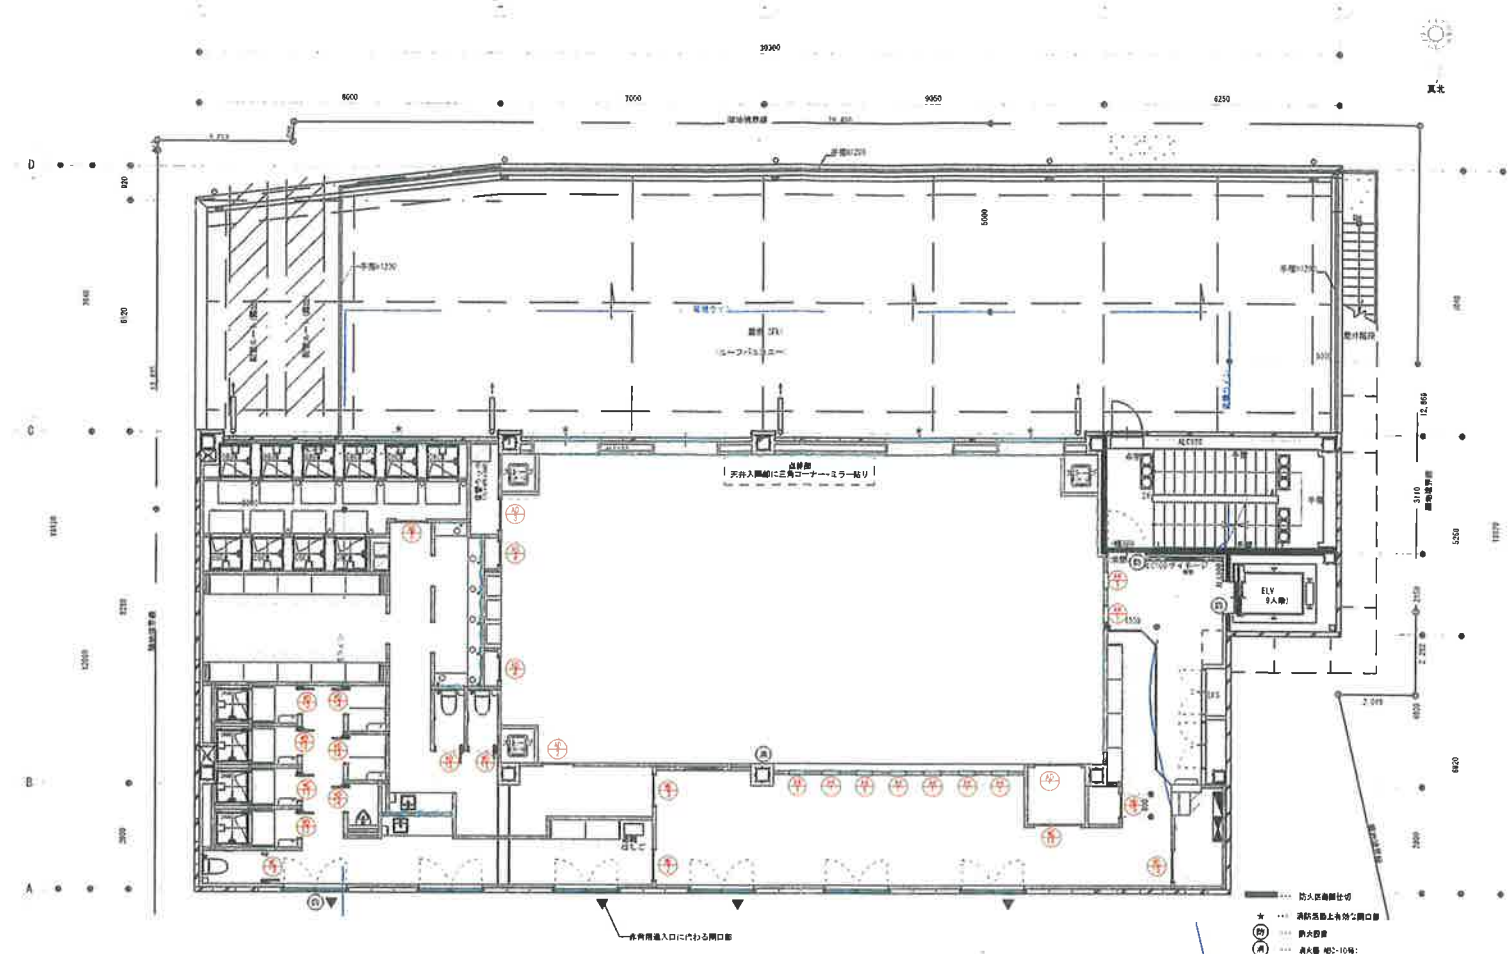

Revised Date

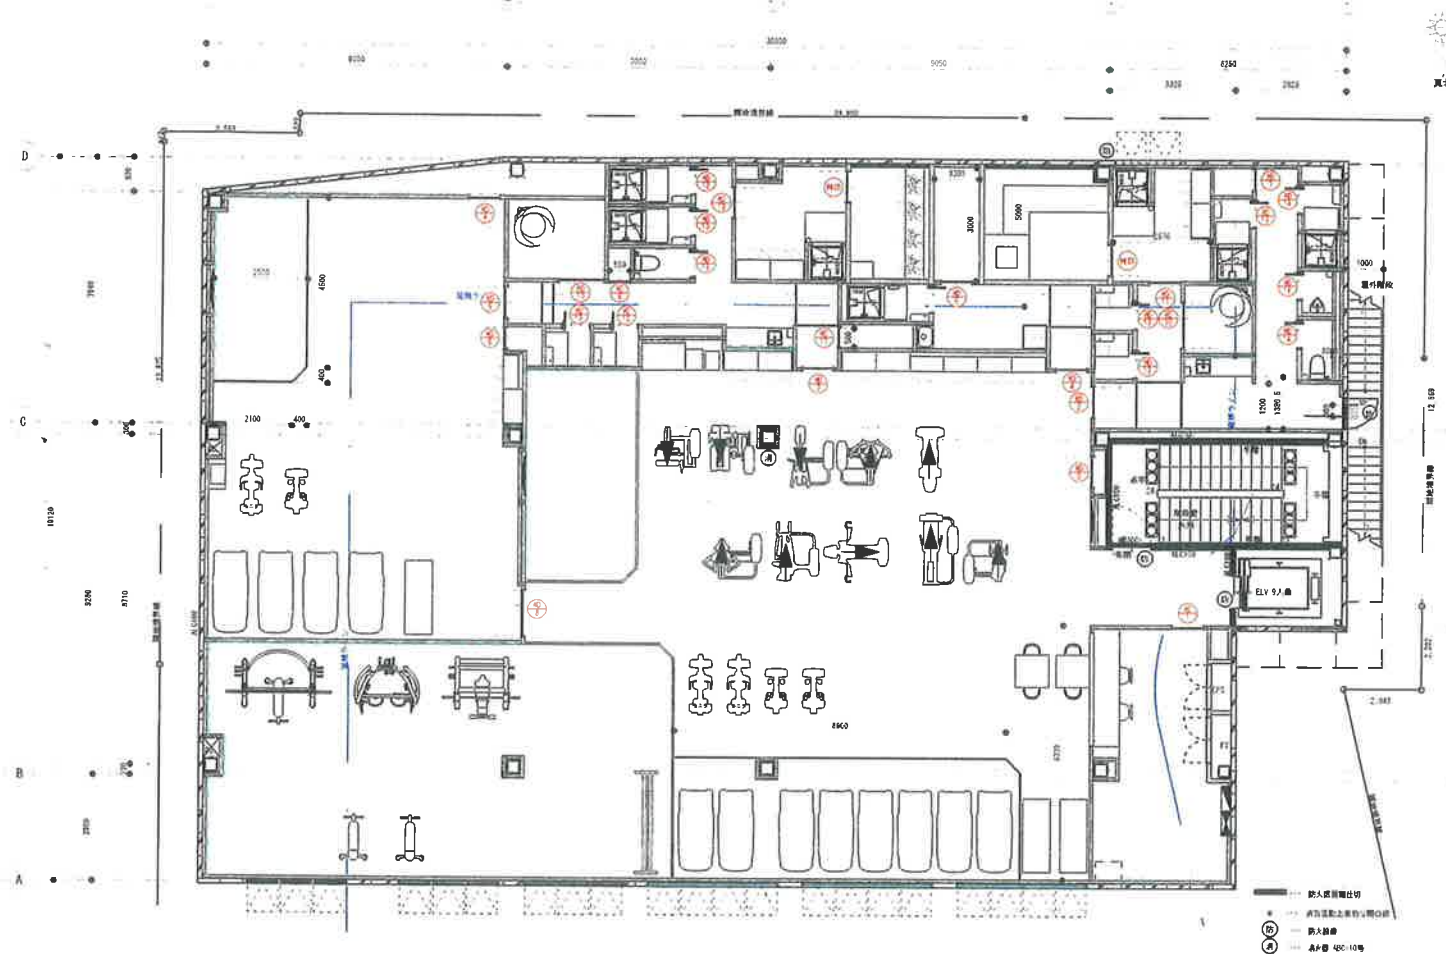

株式会社 C&Pマネジメント
2F AKASAKA-BT BLDG.
1-4-8AKASAKA, MINATO-KU, TOKYO
〒107-0052 TEL: 03-5575-5213/FAX: 03-5575-5214
URL <http://www.cm-pm.jp>

PROJECT : (仮称) JOYFIT24経堂 新装工事	TITLE : 建具プロット図	No : A-24
CHECK :	SCALE : S=1/200	DATE : 2017. 03. 15