


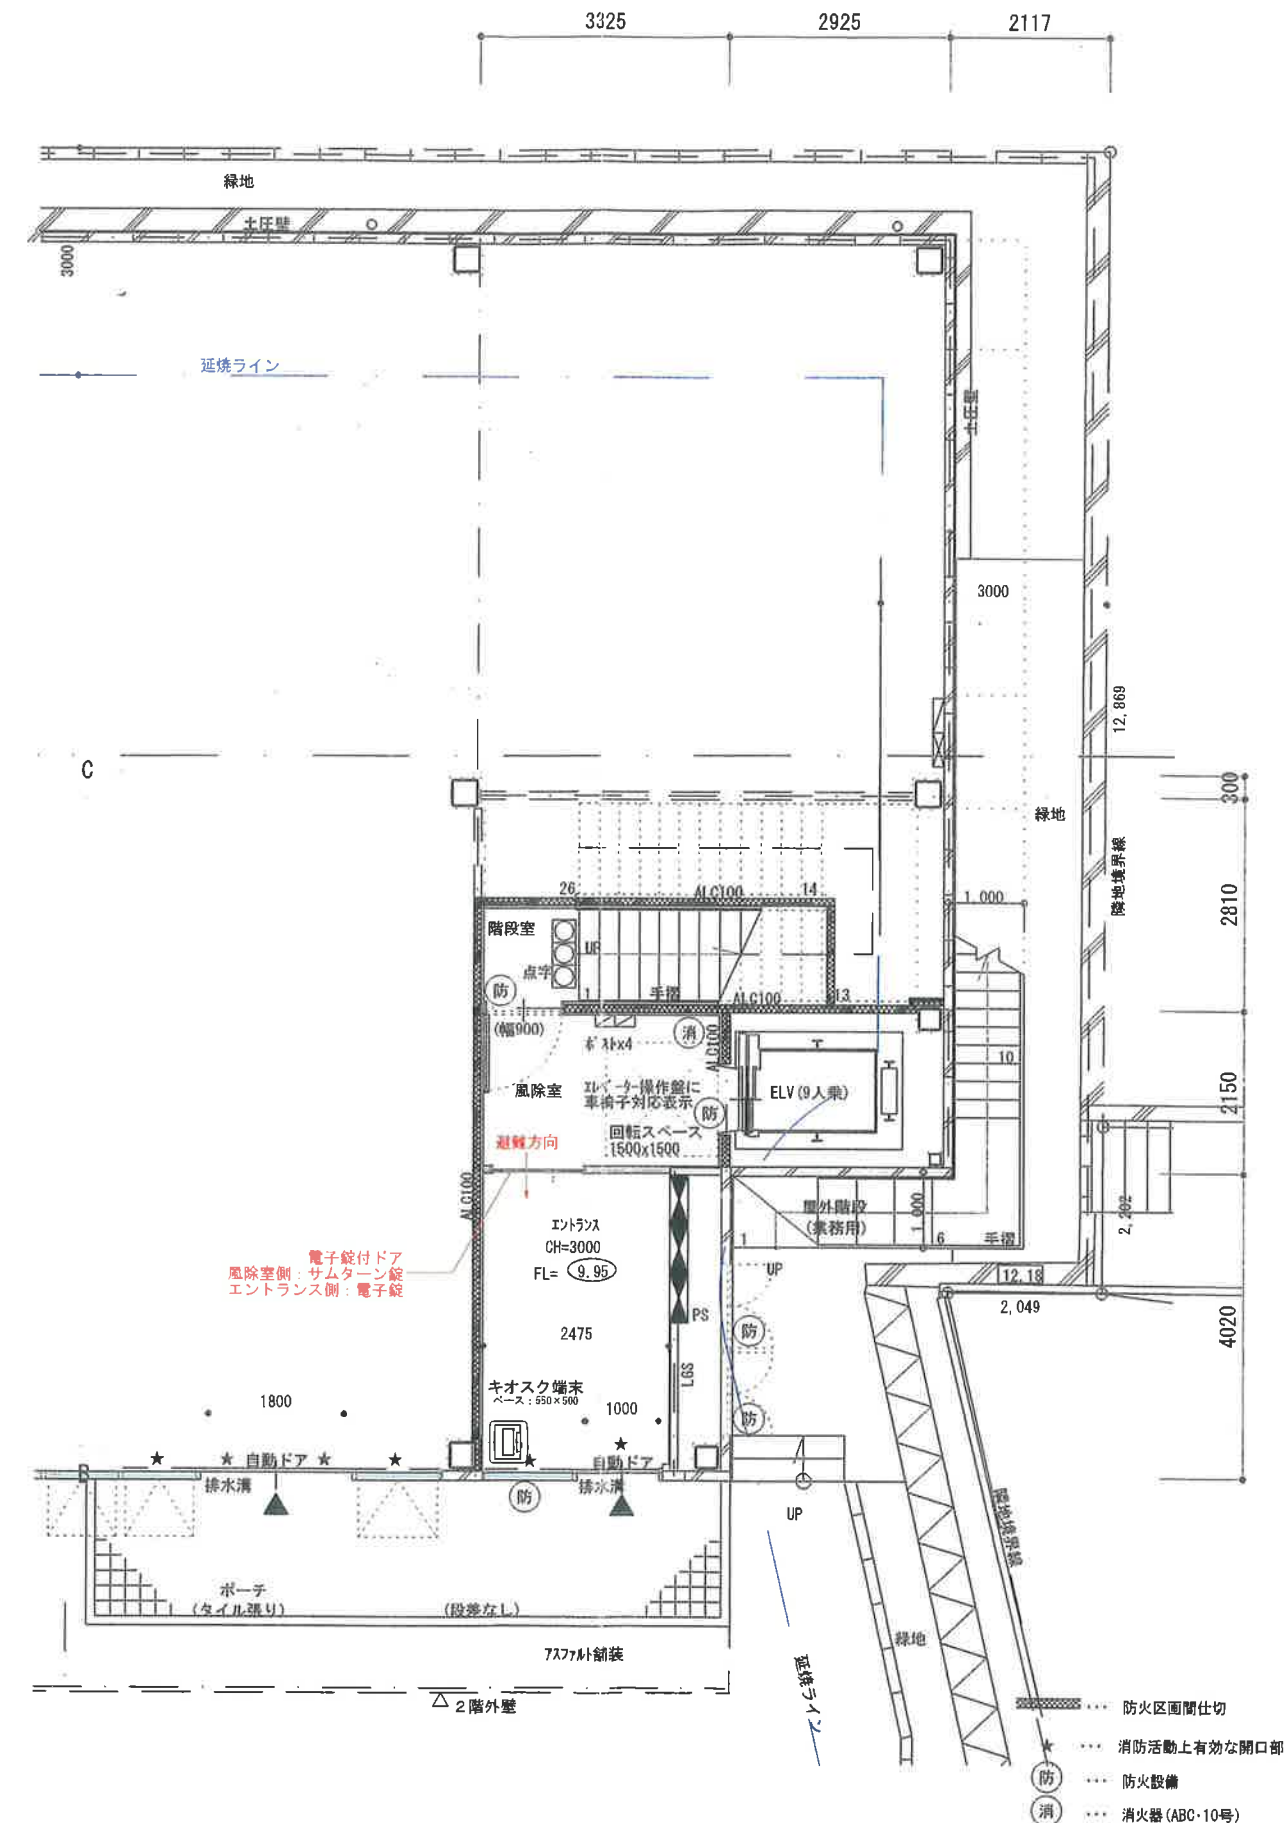

凡例	
MI	ミラー貼り
G	ガラス有・ガラス戸
掃	掃除用具入れ
収	収納

Revised Date	C&P MANAGEMENT	株式会社 C&Pマネジメント 2F AKASAKA-BT BLDG. 1-4-BAKASAKA, MINATO-KU, TOKYO 〒107-0052 TEL: 03-5575-5213/FAX: 03-5575-5214 URL http://www.cm-pm.jp	PROJECT	(仮称) JOYFIT24経堂 新装工事	TITLE	1F: 平面図	No	A-05
			CHECK		SCALE	S=1/100	DATE	2017. 03. 15