


1 2 3 4 5

8000 7000 30300 9050 6250 3425 2925

真北

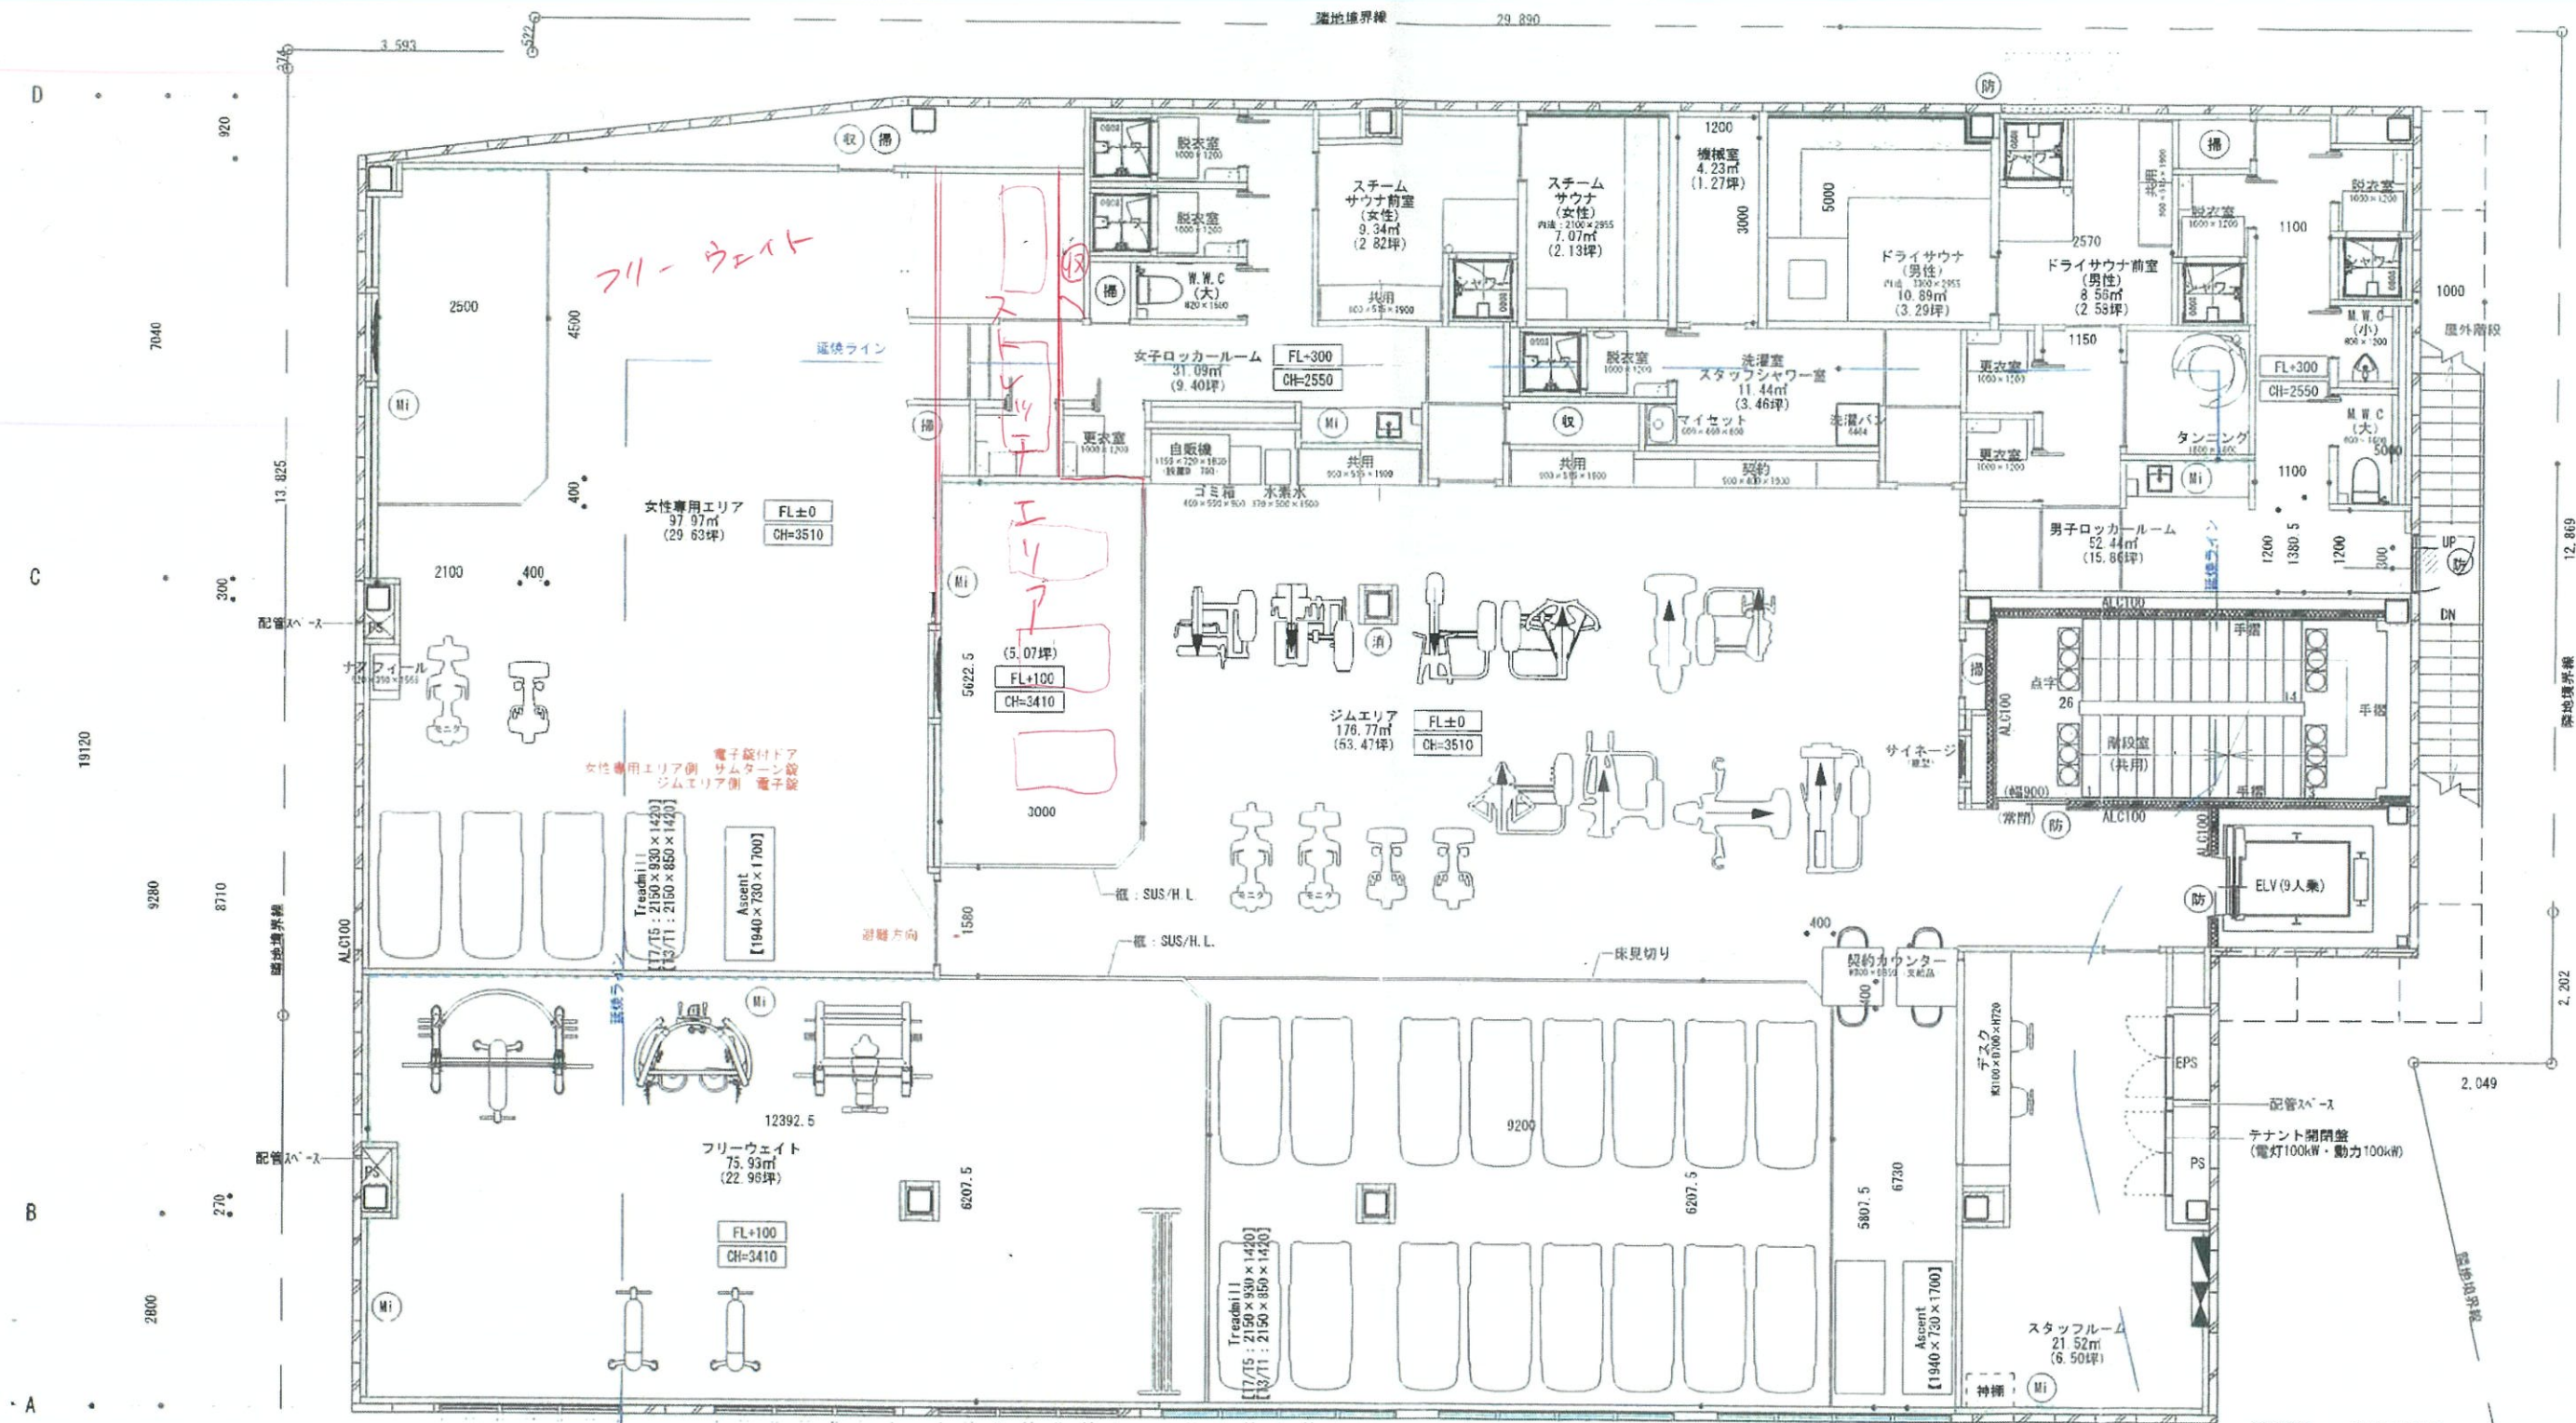

| 凡例  |           |
|-----|-----------|
| (ミ) | ミラー貼り     |
| (G) | ガラス有・ガラス戸 |
| (掃) | 掃除用具入れ    |
| (収) | 収納        |

|                           |                      |
|---------------------------|----------------------|
| 店舗面積<br>(共用階段、ELV除く現況内寸法) | 158.87坪<br>(526.21㎡) |
| 積載荷重 400kg/㎡              |                      |
| ※合計面積は賃貸契約面積と違ってきます。      |                      |

|                            |   |                              |               |          |
|----------------------------|---|------------------------------|---------------|----------|
| 2017.05.23<br>Revised Date | <b>C&amp;P MANAGEMENT</b><br>株式会社 C&Pマネジメント<br>2F AKASAKA-BT BLDG.<br>1-4-8AKASAKA, MINATO-KU, TOKYO<br>〒107-0052 TEL:03-5575-5213/FAX:03-5575-5214<br>URL: http://www.c&p-m.jp | PROJECT (仮称) JOYFIT24経営 新装工事 | TITLE 2F: 平面図 | No: A-06 |
|                            |   | CHECK                        | SCALE S=1/100 |          |

- ★ ... 消防活動上有効な開口部
- (防) ... 防火設備
- (消) ... 消火器 (ABC・10号)